

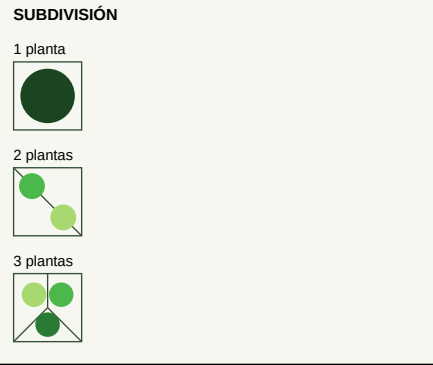


LEYENDA		
S	Cód.	Nombre científico
Canéfitas (<1 m)		
CA01	CA01	Thymus mastichina
CA02	CA02	Thymus zygis subsp. gracilis
CA03	CA03	Thymus capitatus
CA04	CA04	Salvia rosmarinus
CA05	CA05	Lavandula stoechas
CA06	CA06	Lavandula pedunculata
CA07	CA07	Helichthys sibiricus
CA08	CA08	Teucrium capitatum
CA09	CA09	Cistus salvifolius
Microfaner. (1-4 m)		
MI01	MI01	Pistacia lentiscus
MI02	MI02	Myrtus communis
MI03	MI03	Phillyrea angustifolia
MI04	MI04	Cistus ladanifer
MI05	MI05	Viburnum tinus
MI06	MI06	Jasminum fruticosum
MI07	MI07	Ostrya alba
MI08	MI08	Retama monosperma
MI09	MI09	Tamarix africana
MI10	MI10	Tamarix canariensis
MI11	MI11	Chamaecyparis humilis
Mesofaner. (3-10 m)		
ME01	ME01	Olea europaea
ME02	ME02	Punica granatum
ME03	ME03	Laurus nobilis
ME04	ME04	Tamarix gallica
ME05	ME05	Arbutus unedo
ME06	ME06	Cercanopia saligna
ME07	ME07	Pyrus bourgaiana
ME08	ME08	Prunus dulcis
Megafaner. (8-30 m)		
MG01	MG01	Quercus ilex subsp. ballota
MG02	MG02	Quercus faginea
MG03	MG03	Quercus suber
MG05	MG05	Pinus halepensis
MG06	MG06	Cedrus australis
MG07	MG07	Ulmus minor
MG09	MG09	Acer monspessulanum
MG10	MG10	Populus alba
MG11	MG11	Populus nigra

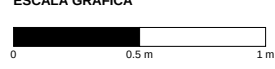

Escala 1:30 - 1 célula = 1x1 m²

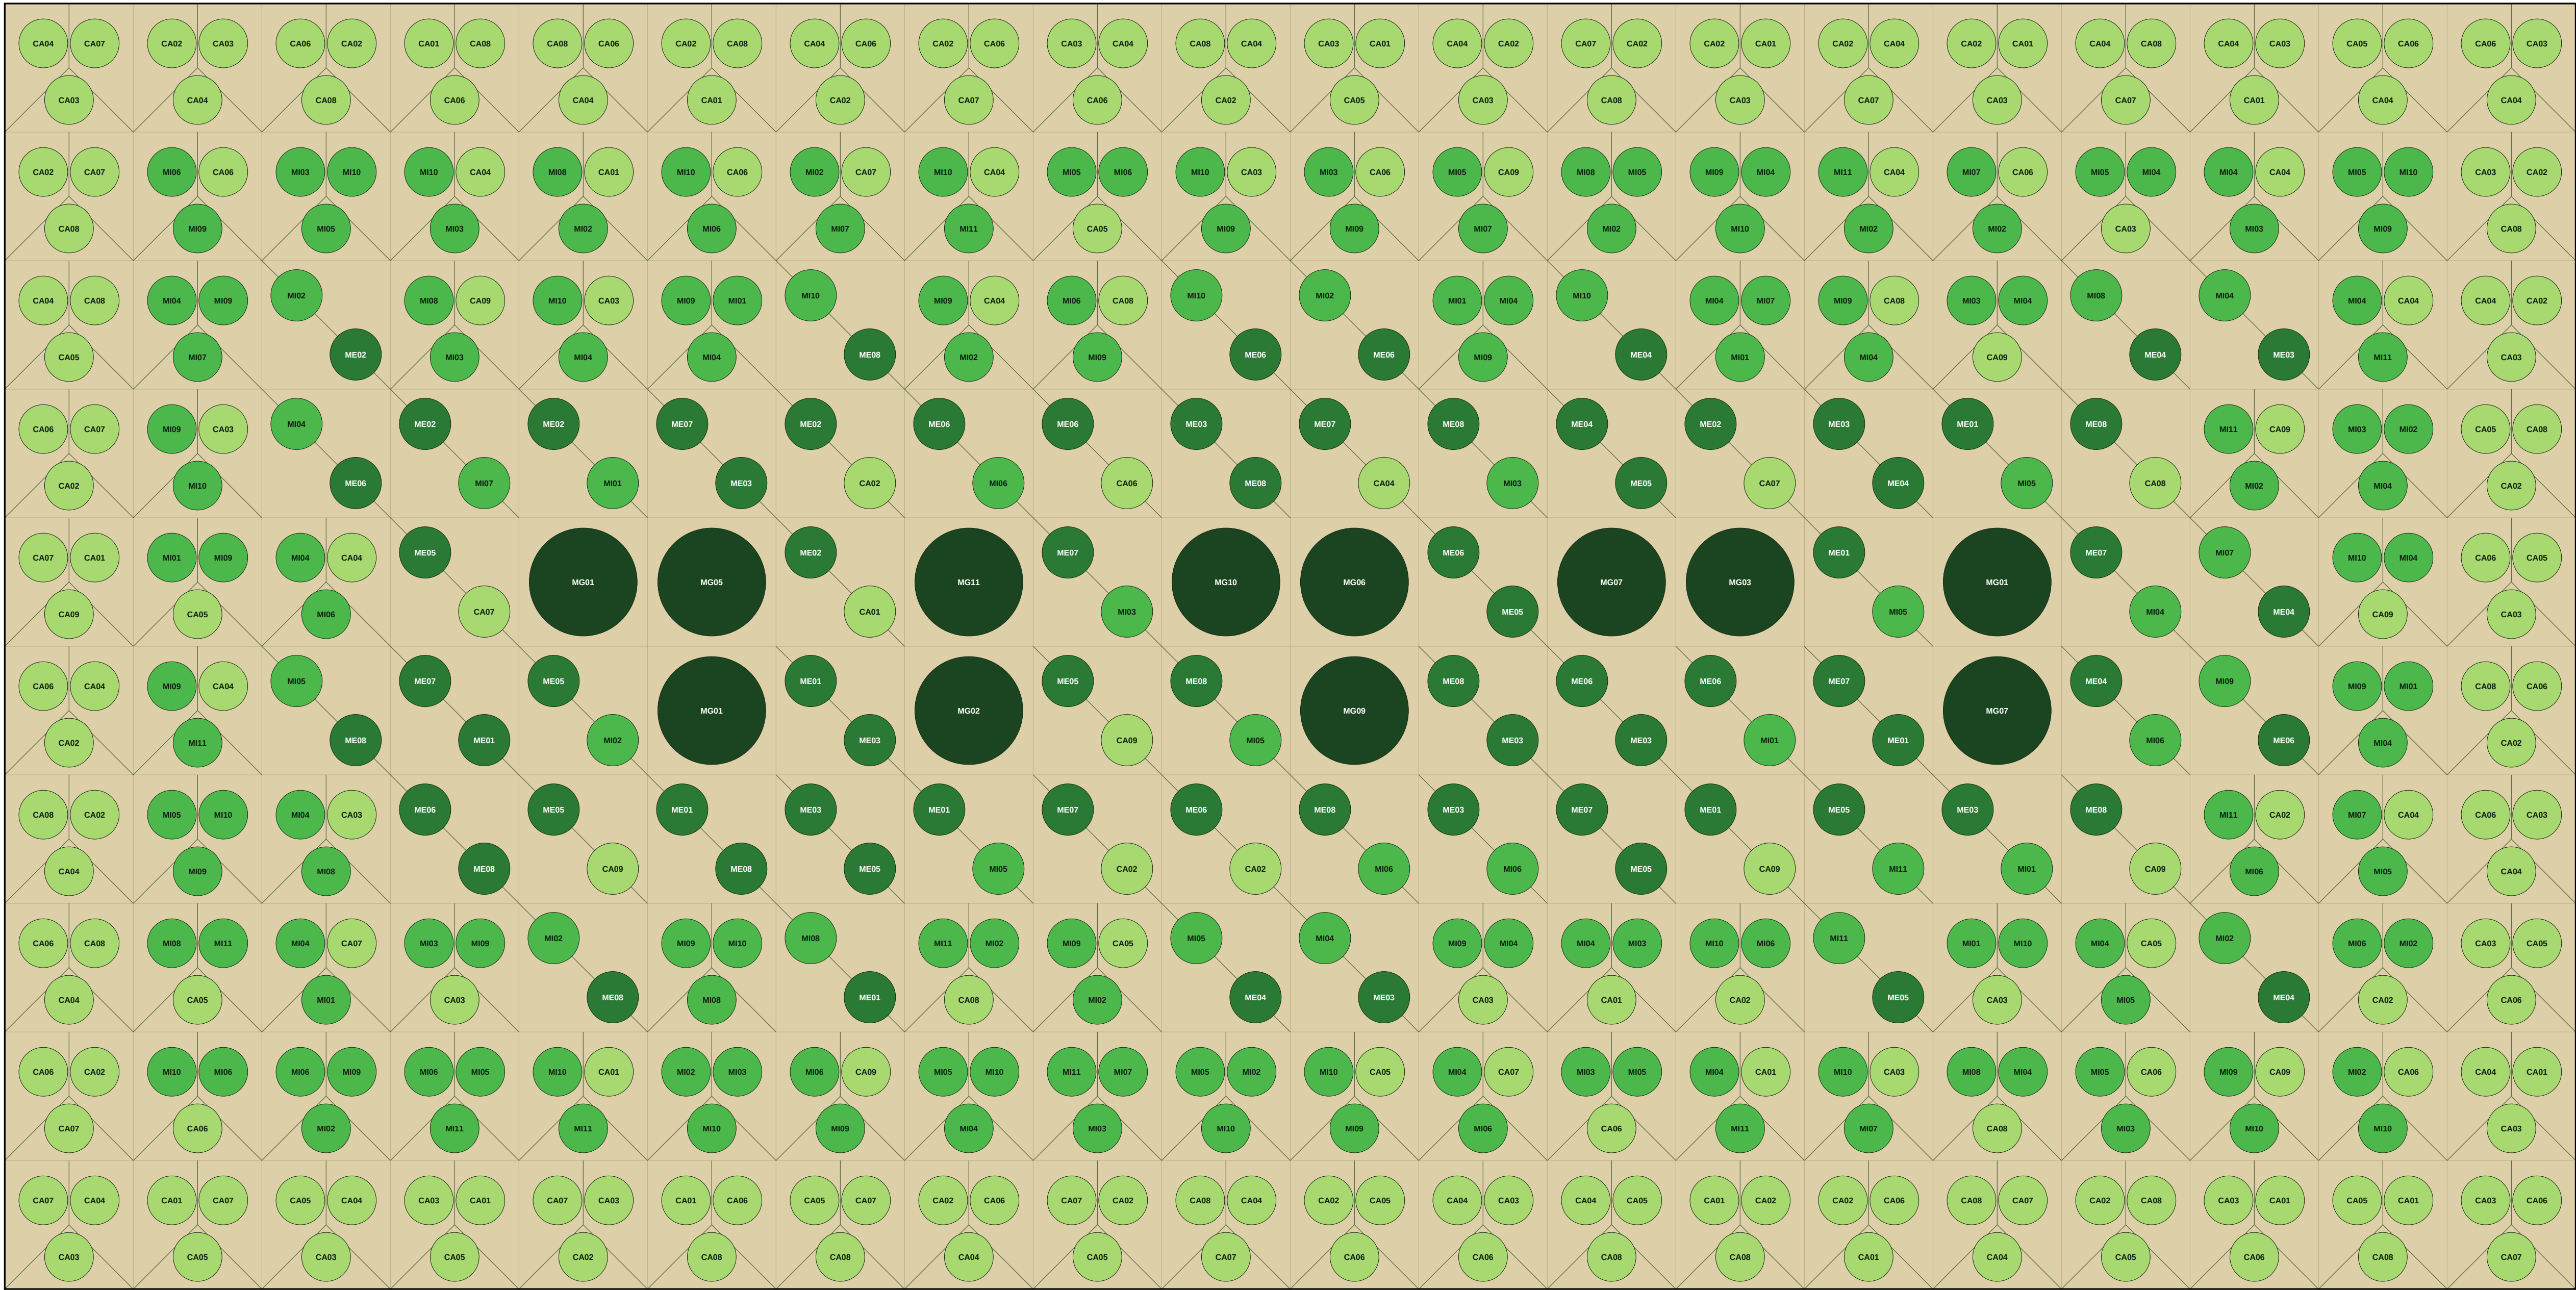

PLANO DE PLANTACIÓN — HyphaPod Piloto		
Microhospicio urbano - Método Miyawaki		
PROYECTO	UNIVERSIDAD	W PLANO
Mycoroots — TFG Ingeniería Agroalimentaria	Universidad de Córdoba	01
AUTORA		ESCALA
Ana Velasco Márquez		1:30
FECHA	TOTAL PLANTAS	FORMATO
2026	515 ud.	DIN A1 (841x594 mm)